


AREA STATEMENT		
PLOT AREA = 7333.22 SQYD		
ROAD AREA = 1968.10 SQYD		
TOTAL AREA = 5365.12 SQYD		

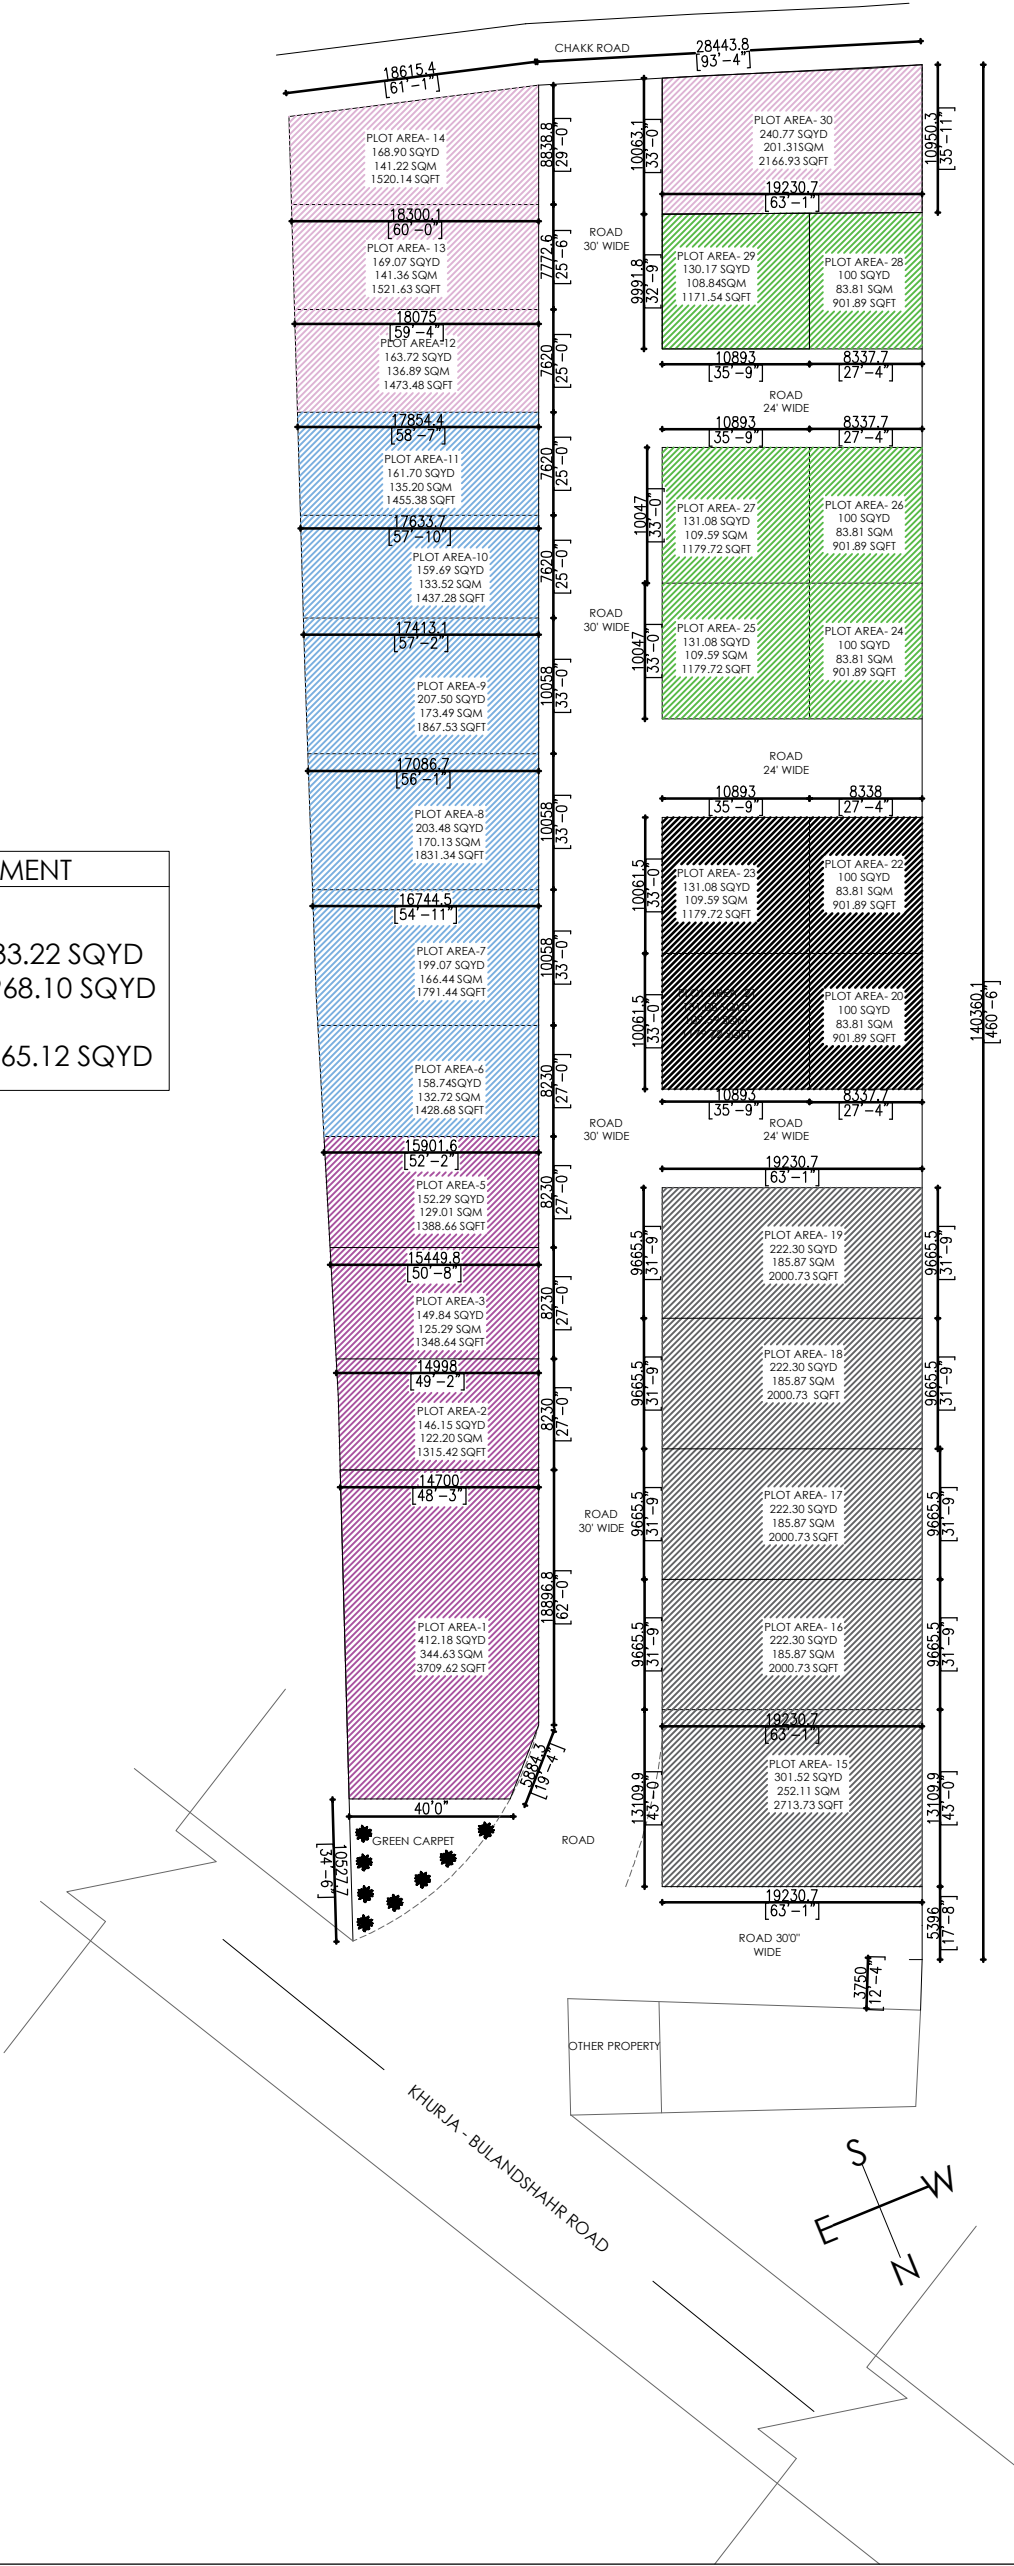

REVISE:		
DATE:	REASON:	BY:
09-04-2023	G.F.C.	VISHAL

- GENERAL NOTES
- THIS DRAWING IS THE COPYRIGHT OF SPARSH GUPTA ARCHITECTS' AND CANNOT BE RETAINED, COPIED OR USED IN ANY FORM WITHOUT THE ABOVE CONSULTANTS CONSENT.
 - DO NOT SCALE FROM THE DRAWINGS.
 - ONLY WRITTEN DIMENSIONS ARE TO BE FOLLOWED.
 - THIS DRAWING HAS TO BE READ IN CONJUNCTION WITH OTHER RELEVANT ARCHITECTURAL, STRUCTURAL, MECHANICAL, ELECTRICAL, CIVIL DRAWINGS AND ALL RELEVANT SECTIONS OF THE SPECIFICATIONS.
 - DISCREPANCY IF ANY, HAS TO BE BROUGHT TO THE NOTICE OF THE CONSULTANT IMMEDIATELY.

DRAWN BY:	DEEPAK
CHECKED BY:	Ar. SPARSH GUPTA
PROPOSED PLOTTING	

CLIENT:	Mr. RAVINDRA KUMAR
SITE:	KHURJA ROAD BULANDSHAHR, UTTAR PRADESH

ARCHITECT:	SGG architects
HEAD OFFICE:	A-597, SECTOR-46, NOIDA, U.P.
BRANCH OFFICE:	SHOP NO. 94, DEPUTY GANJ, BULANDSHAHR, U.P.
Ph :	+91-9411960694
EMAIL:	SPARSHGUPTAARCHITECTS@GMAIL.COM